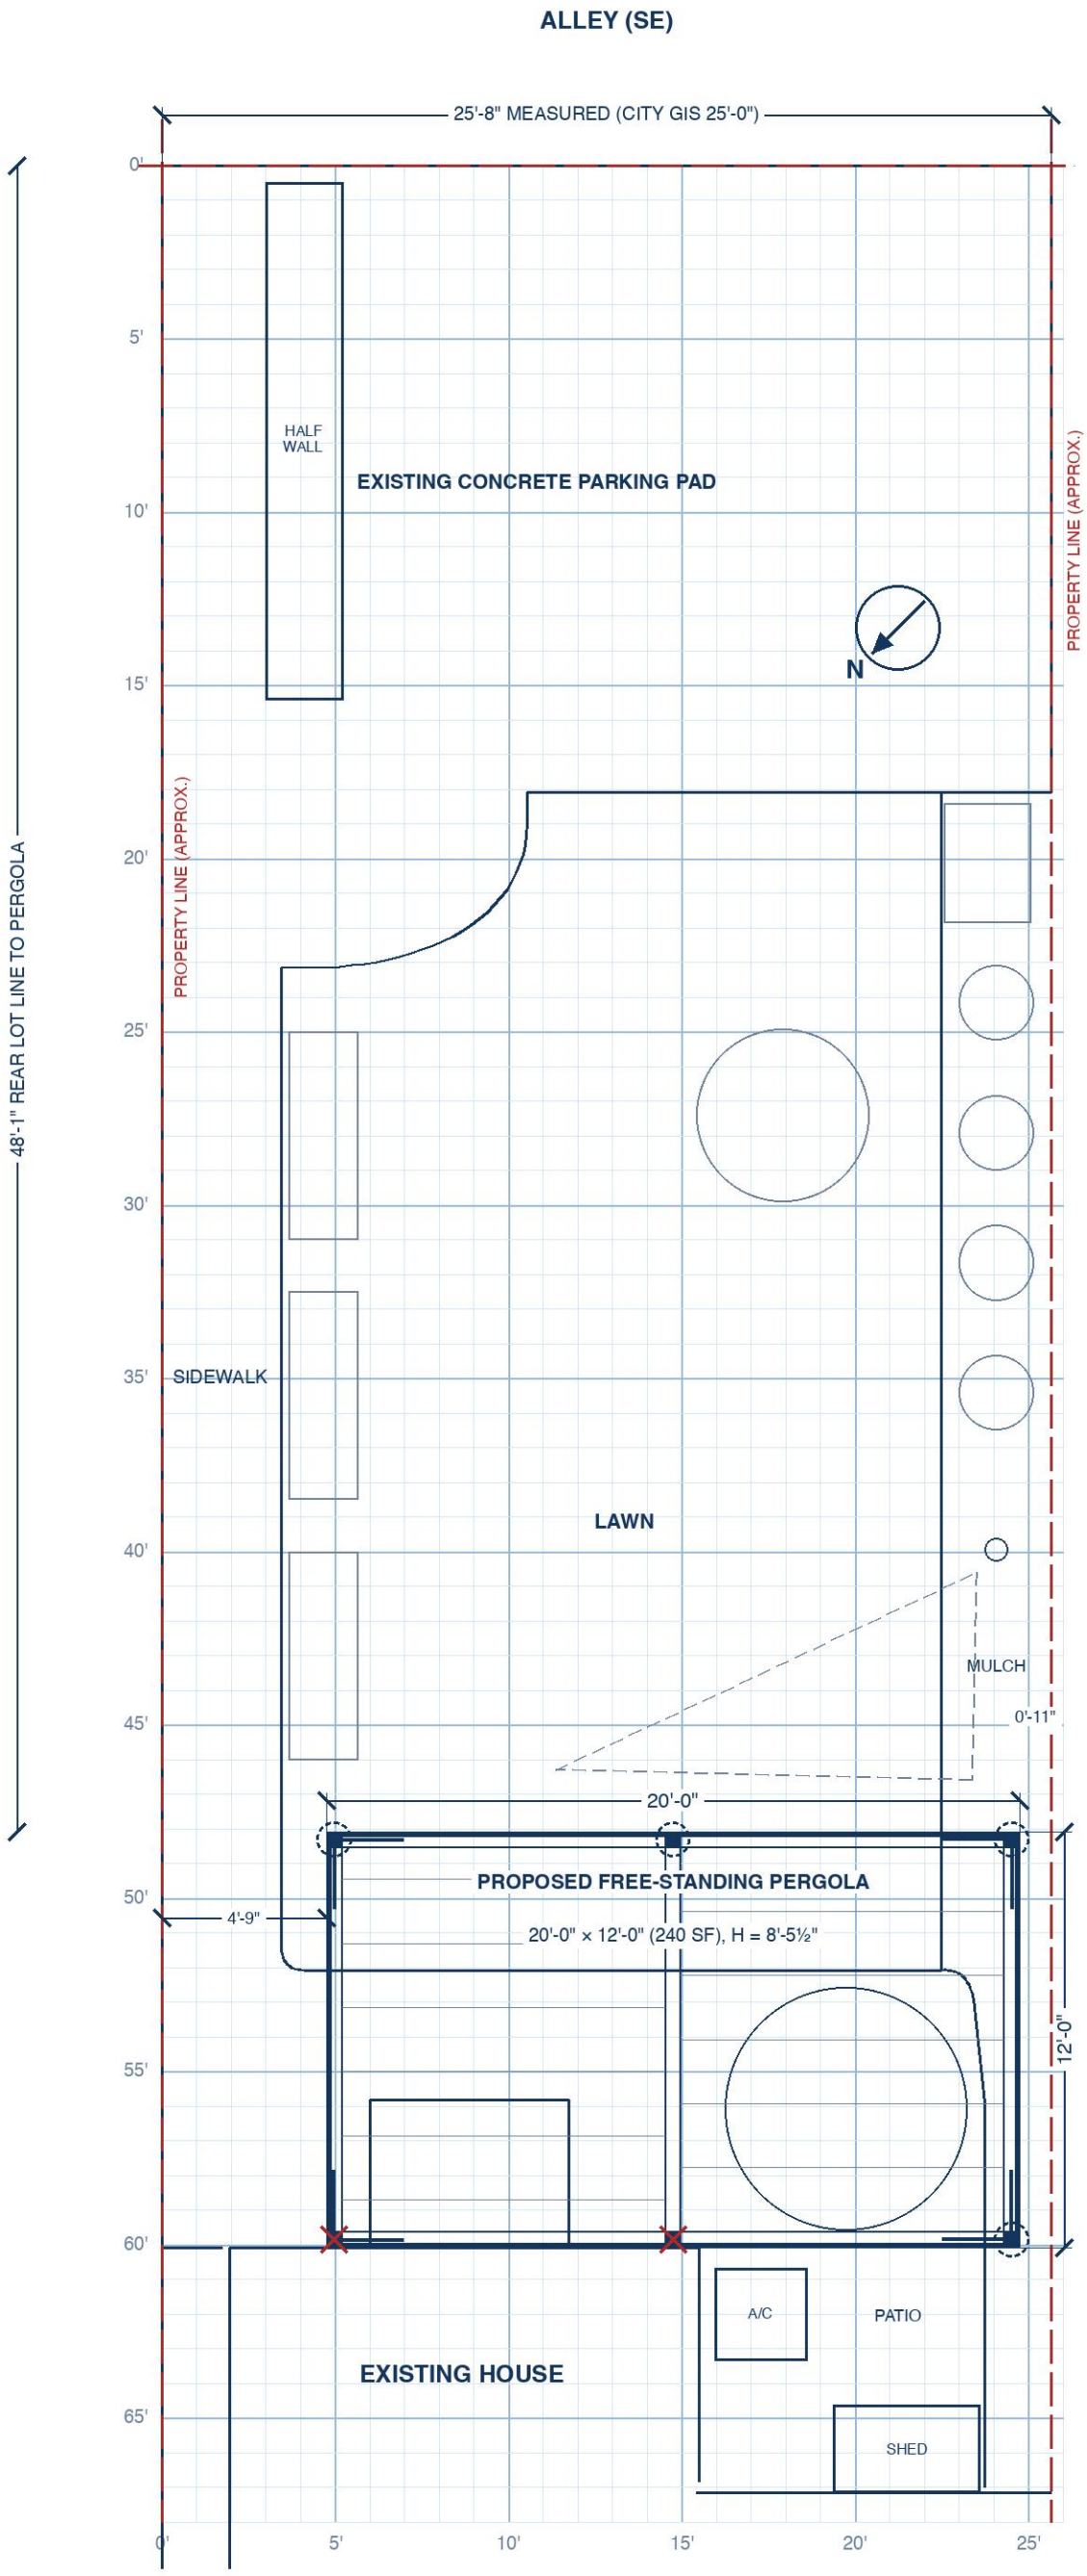



SITE PLAN (REAR YARD)

SCALE: 3/16" = 1'-0" GRID: 1'-0" SQUARES, HEAVY EVERY 5'-0"
GRID ORIGIN: REAR (NE) LOT CORNER. UP = SE (ALLEY).

0' 5' 10'


FRONT ELEVATION (FROM YARD)

SCALE: 1/8" = 1'-0"

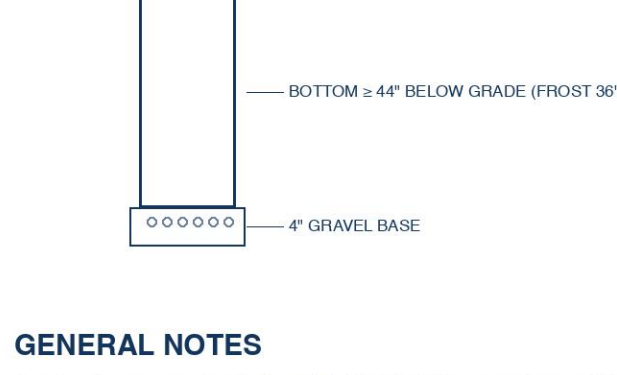

12" DIA. CONCRETE PIERS (DASHED); 2 REAR POSTS ON EXISTING SLAB
2x6 ROOF SLATS @ ±11" O.C. AT 45° SIT BETWEEN BEAMS (NOT SHOWN)

PIER DETAIL (N.T.S.)

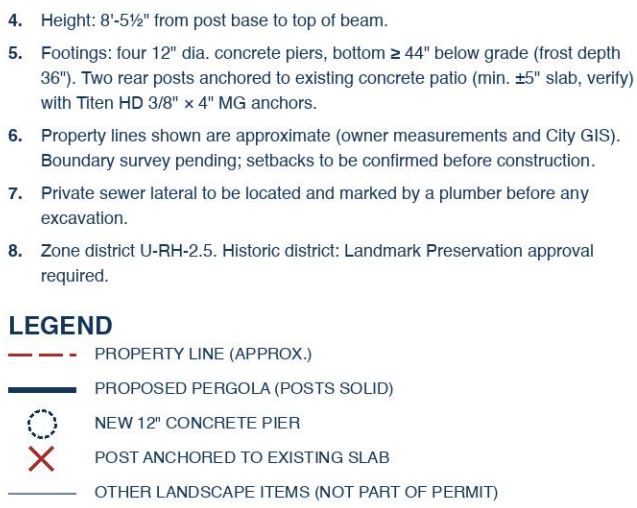

GENERAL NOTES

1. Free-standing pergola, 20'-0" × 12'-0" (240 SF). Kit: Zen Pergolas 6x6, 2-block, free-standing.
2. Posts & beams: 6x6 #1 Douglas fir (5½" × 5½"), FOHC, factory stained. Posts 96"; beams on top.
3. Roof: open 2x6 slats at 45°, ±11" o.c., 11 per opening. Bracing: eight 6x6 knee braces, 30".
4. Height: 8'-5½" from post base to top of beam.
5. Footings: four 12" dia. concrete piers, bottom ≥ 44" below grade (frost depth 36"). Two rear posts anchored to existing concrete patio (min. ±5" slab, verify) with Titen HD 3/8" × 4" MG anchors.
6. Property lines shown are approximate (owner measurements and City GIS). Boundary survey pending; setbacks to be confirmed before construction.
7. Private sewer lateral to be located and marked by a plumber before any excavation.
8. Zone district U-RH-2.5. Historic district: Landmark Preservation approval required.

LEGEND

- PROPERTY LINE (APPROX.)
- PROPOSED PERGOLA (POSTS SOLID)
- NEW 12" CONCRETE PIER
- POST ANCHORED TO EXISTING SLAB
- OTHER LANDSCAPE ITEMS (NOT PART OF PERMIT)

PROJECT	**REAR YARD PERGOLA — DENVER PROPERTY**
ADDRESS	_____
OWNER	_____
SHEET	**A-1 SITE PLAN, PERGOLA ELEVATION & PIER DETAIL**
SCALES	PLAN 3/16" = 1'-0" ELEVATION 1/8" = 1'-0" DETAIL N.T.S.
DATE	2026-10-18 PREPARED BY OWNER SHEET 1 OF 1